
| No. | Reason and Description of Revision | | Revised by / Date / Reviewed by | | Date |
|---|---|---|---|---|---|
| | | | | | |
| | | | | | |
| | | | | | |

# Process Flow Diagram - 300 t/d Lime Production Line

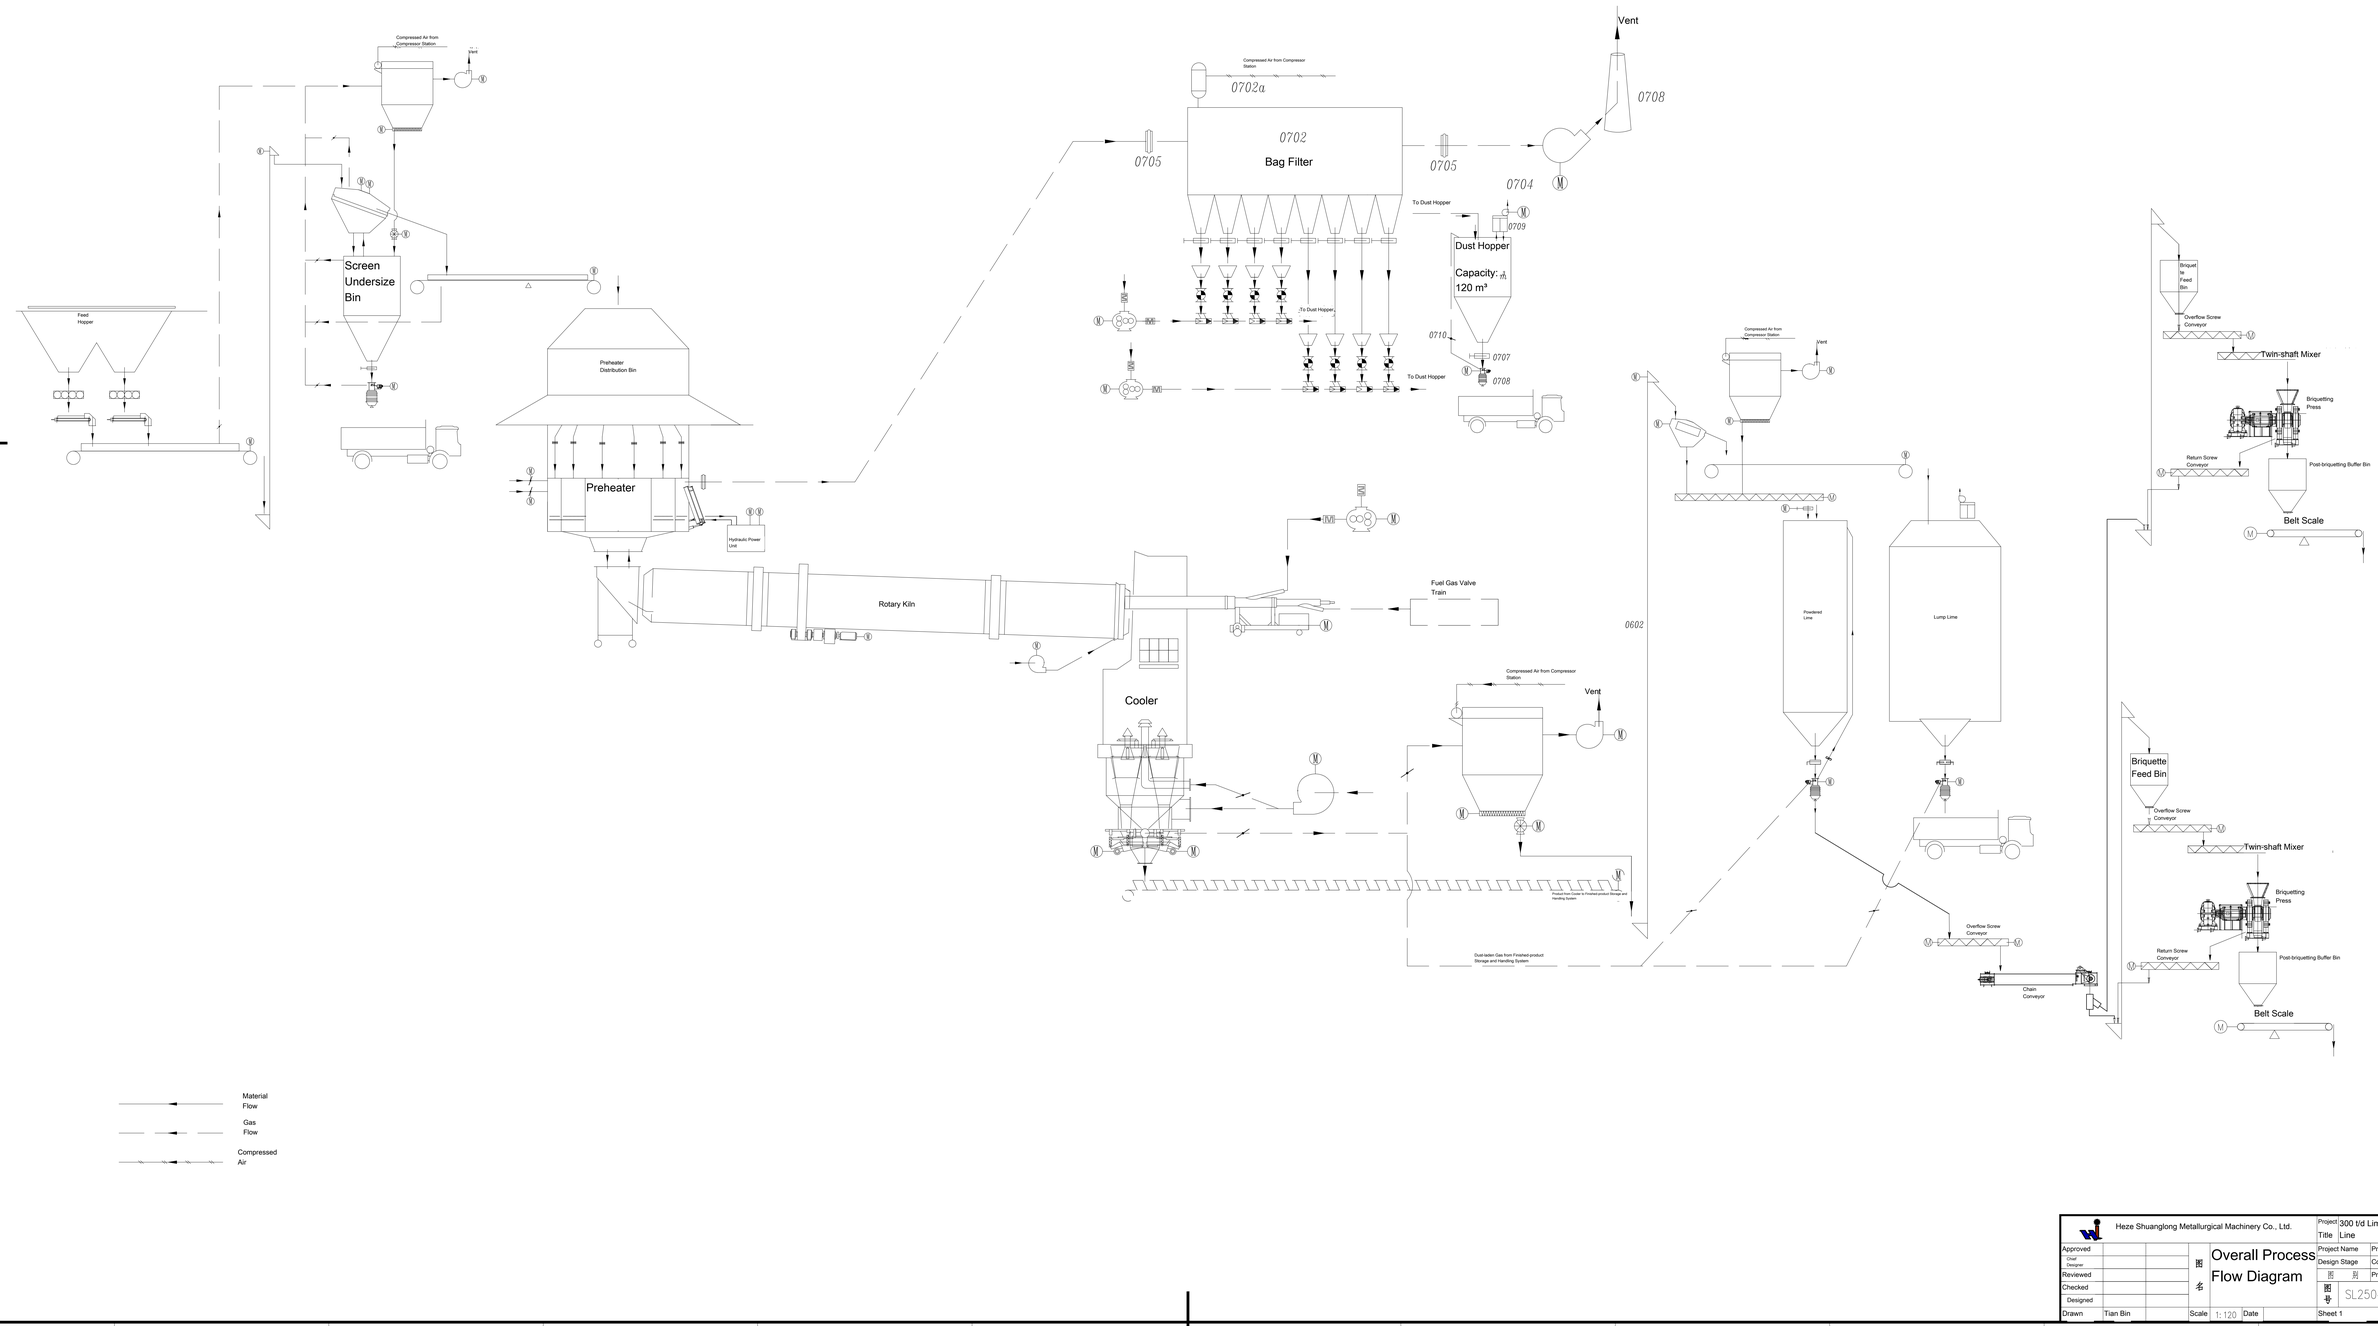


DECLARATION: This work is the property of Heze Shuanglong Metallurgical Machinery Co., Ltd. All information and proprietary technology contained herein are confidential and shall not be copied, duplicated, modified, submitted, or disclosed to any third party without the Company's prior written permission.

| | | | | | |
|---|---|---|---|---|---|
| Heze Shuanglong Metallurgical Machinery Co., Ltd. | | | Project Title | 300 t/d Lime Production Line | |
| Approved | | | 图名 | Overall Process Flow Diagram | Project Name | Process Flow |
| Chief Designer | | | | | Design Stage | Construction Drawing |
| Reviewed | | | | | 图别 | Process |
| Checked | | | | | 图号 | SL2504-GS01-01 |
| Designed | | | | | | |
| Drawn | Tian Bin | | Scale | 1: 120 | Date | Sheet 1 | 1 Sheet Total |